

Revision  
REV 1 PC comments 071723  
REV 2 PC comments 101623  
REV 3 PC comments 010224  
Slab submittal clarification





Architect  
Adolph S. Rosekranz, Inc.  
950 Runnymede Road  
Woodside, CA 94062  
650.851.7201  
Fax 650.851.7202  
rosekranz@pacbell.net

## METAL STUD WALL DETAILS


### TAUBE FAMILY CARRIAGE HOUSE San Mateo County History Museum MUSEUM ADDITION

San Mateo County Historical Association  
2200 Broadway Redwood City, CA 94063  
APN: 052-367-010  
Date 12-20-2022  
Scale U.O.N.  
PRINTED 24X36 AS NOTED  
Job 1702

A5.0  
Sheet

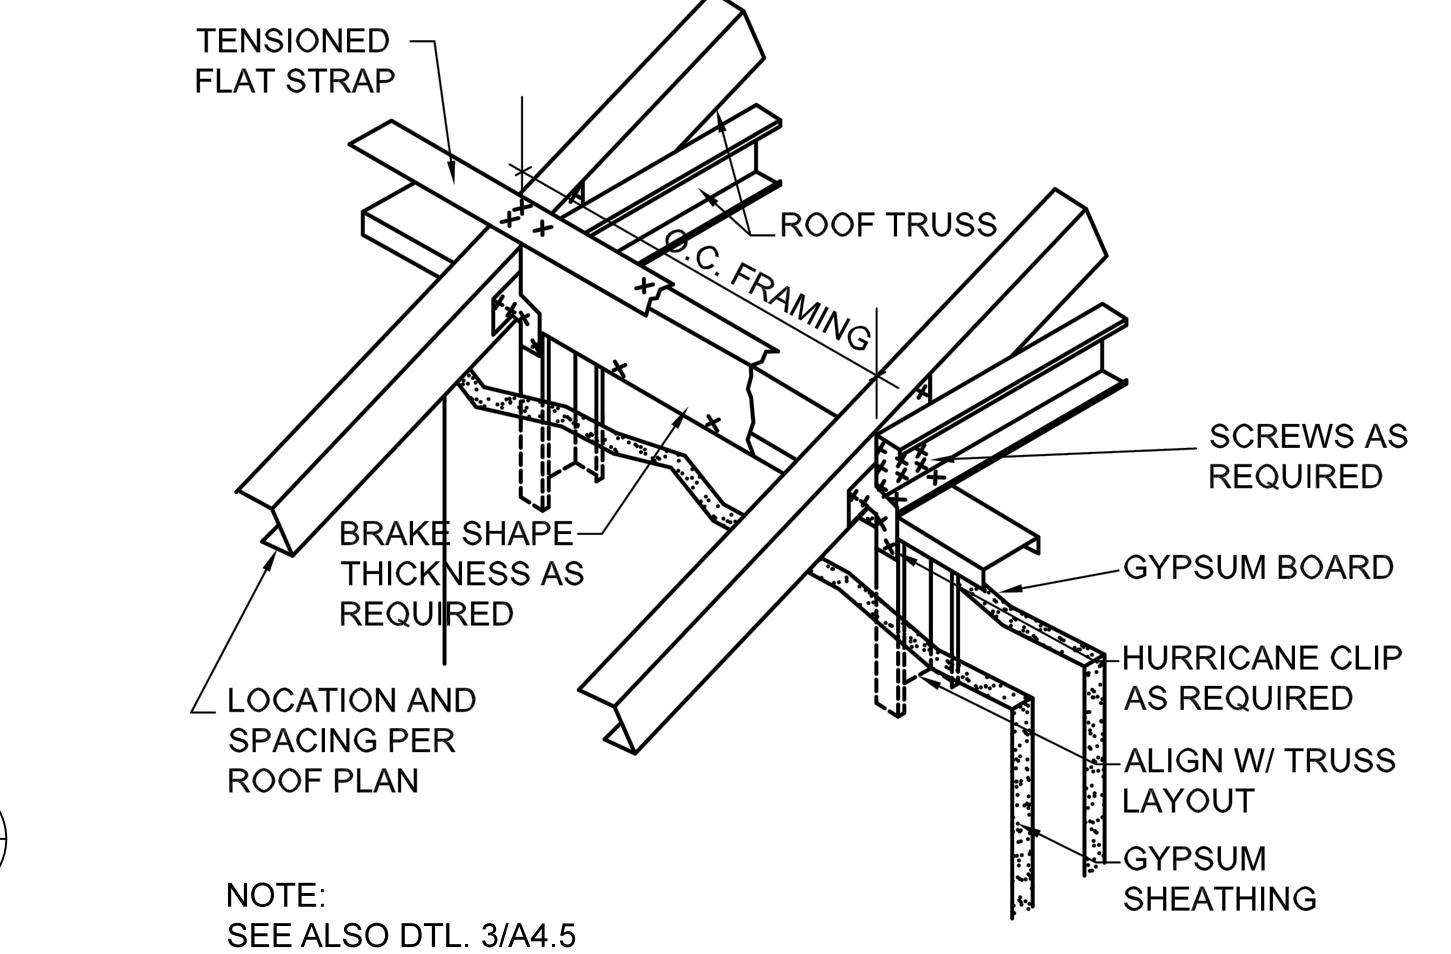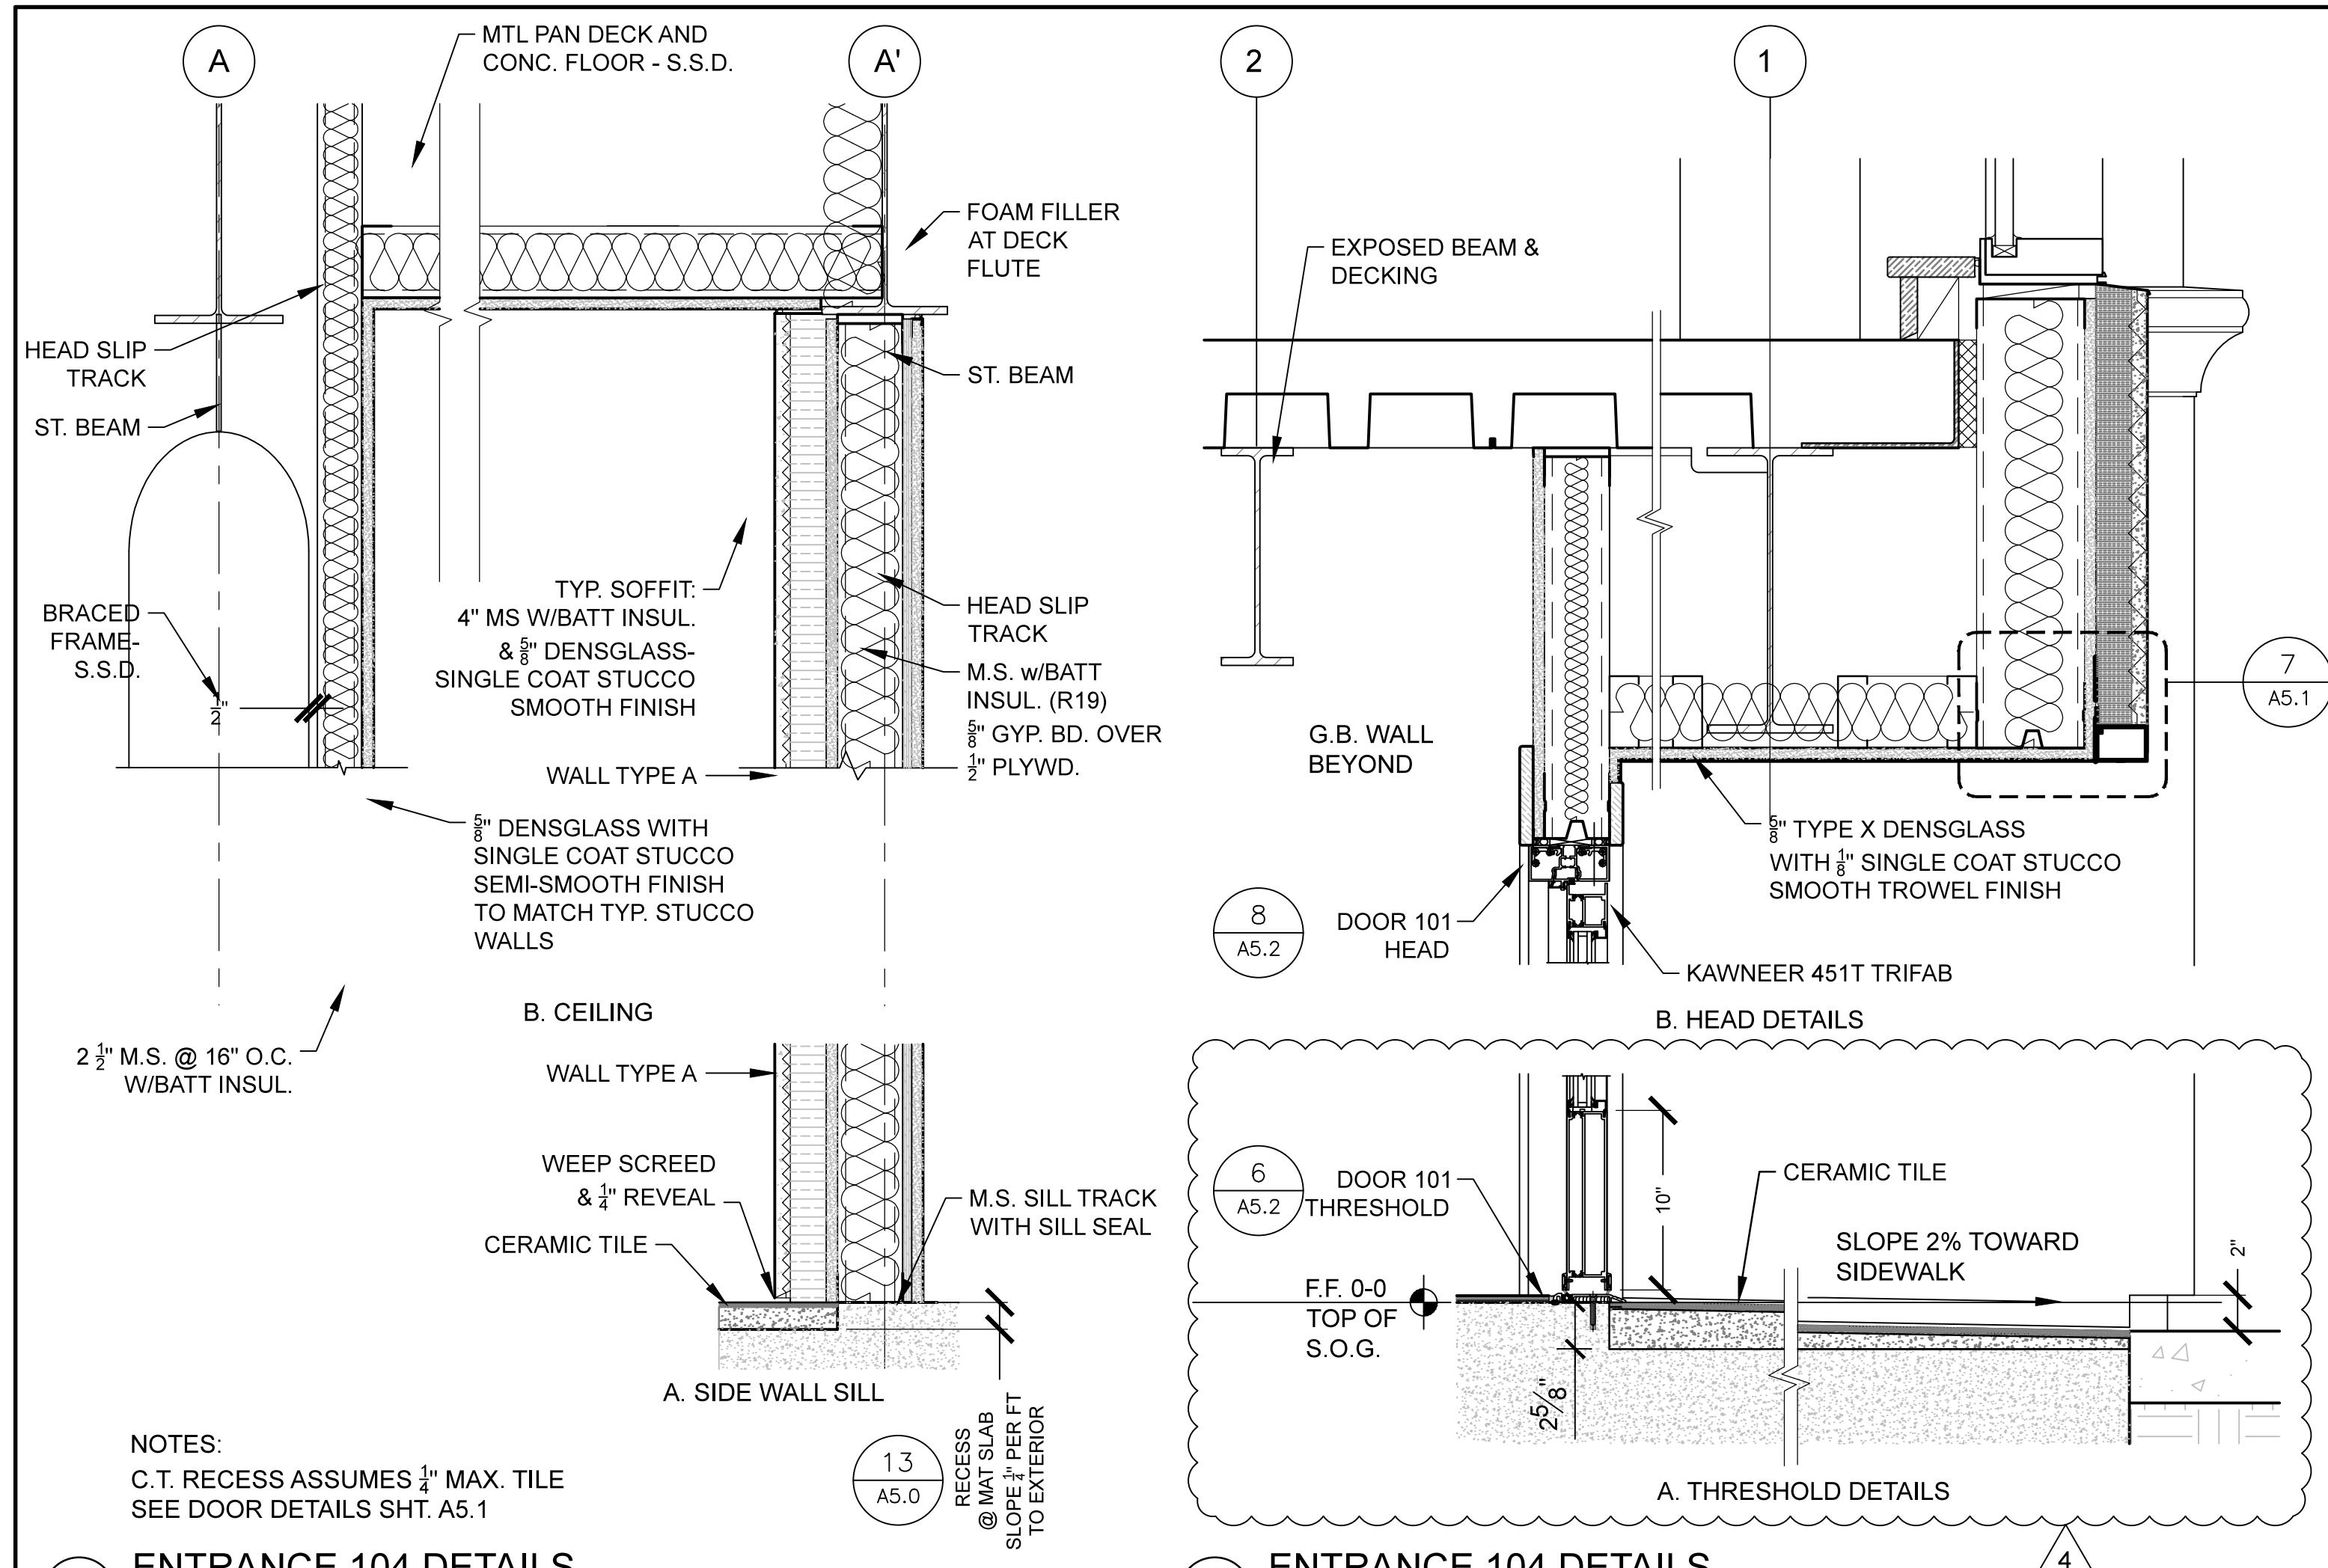


PROVIDE WHERE REQUIRED AT RATED WALLS.  
**CONTROL JOINT AT 1 HOUR FIRE RATED WALL**

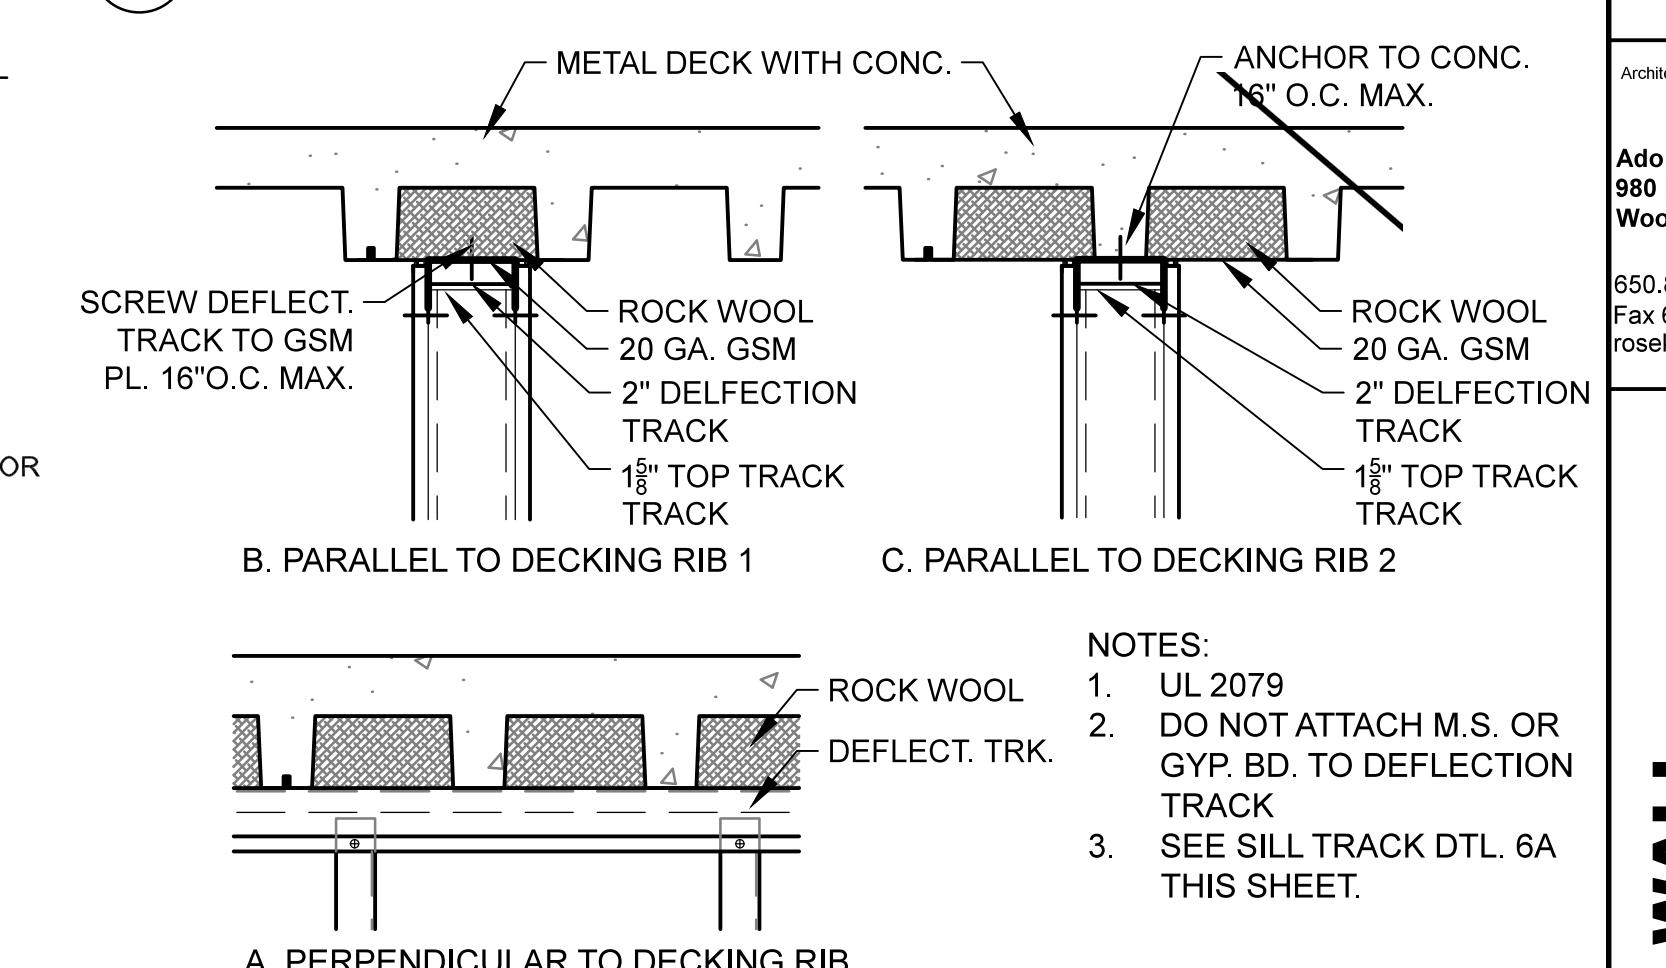


- NOTES:  
1. UL 2079  
2. DO NOT ATTACH M.S. OR GYP. BD. TO DEFLECTION TRACK  
3. SEE SILL TRACK DTL. 6A THIS SHEET.


**TYPICAL PENTHOUSE ROOF M.S. RAFTER DETAIL**

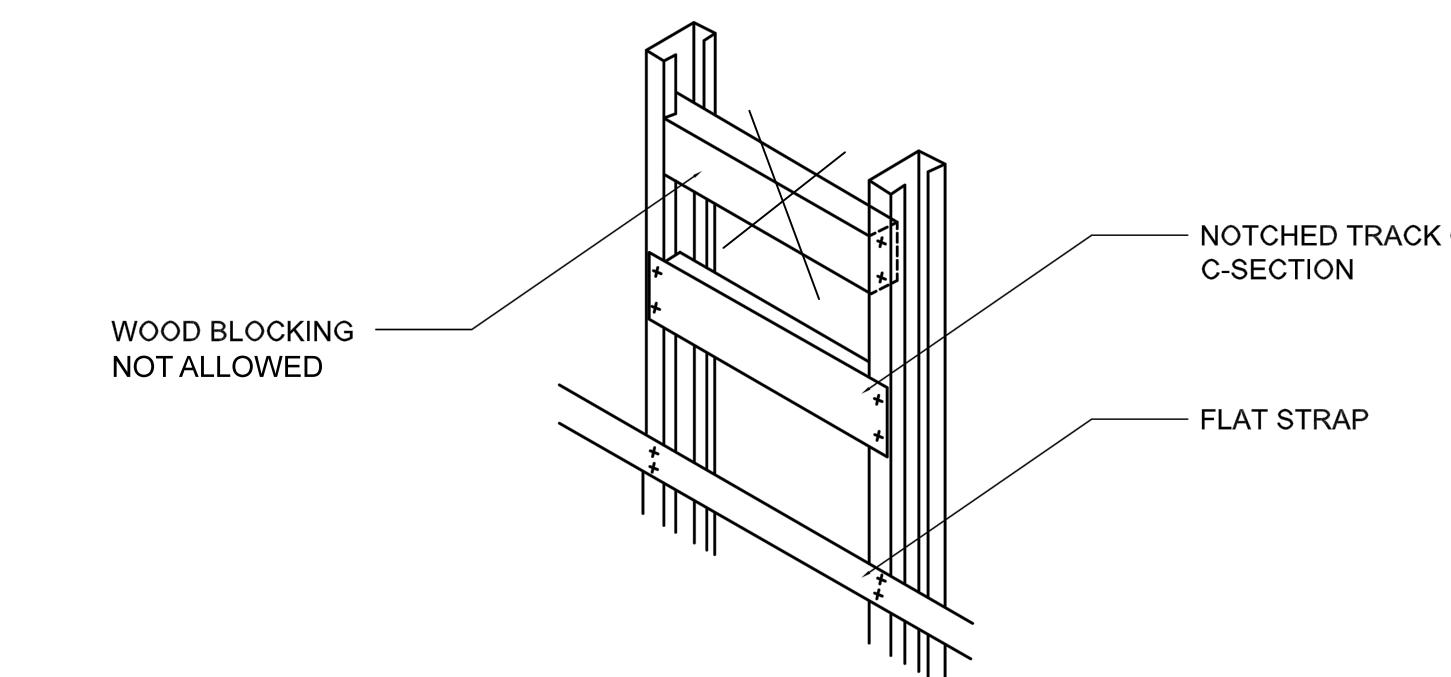


**CABINET BLOCKING DETAIL**

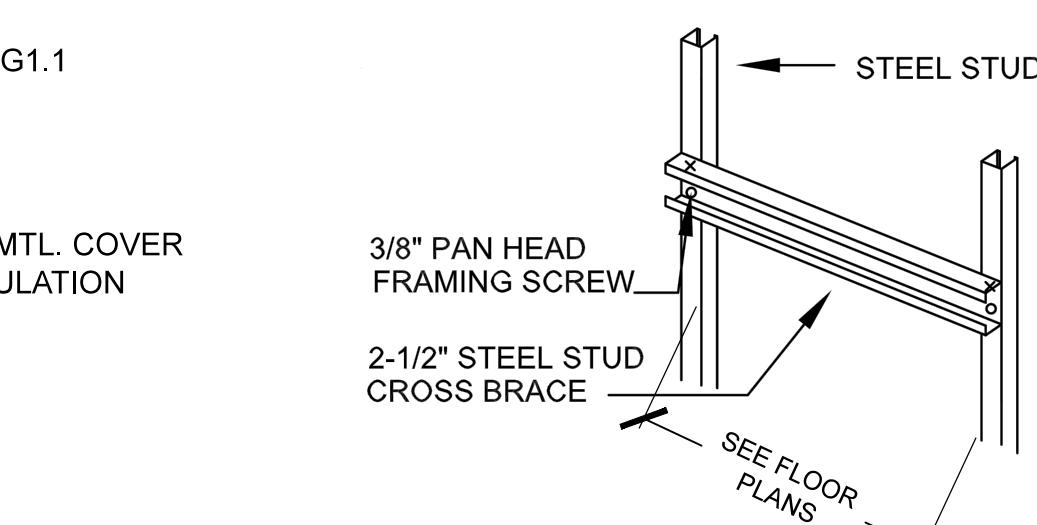


**NEW MTL STUD WALL AT EXISTING WALL TO REMAIN**

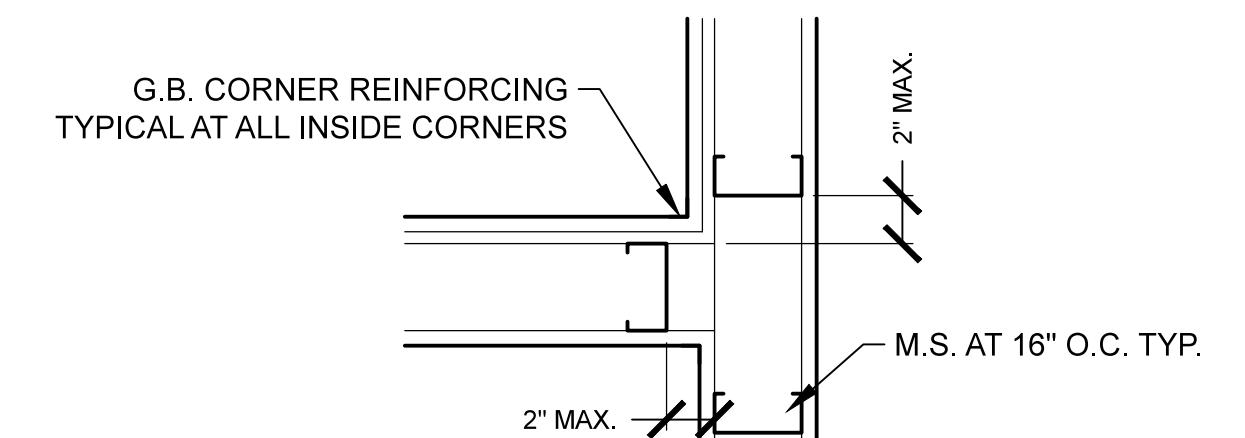

**CHASE WALL METAL STUD BRACE**

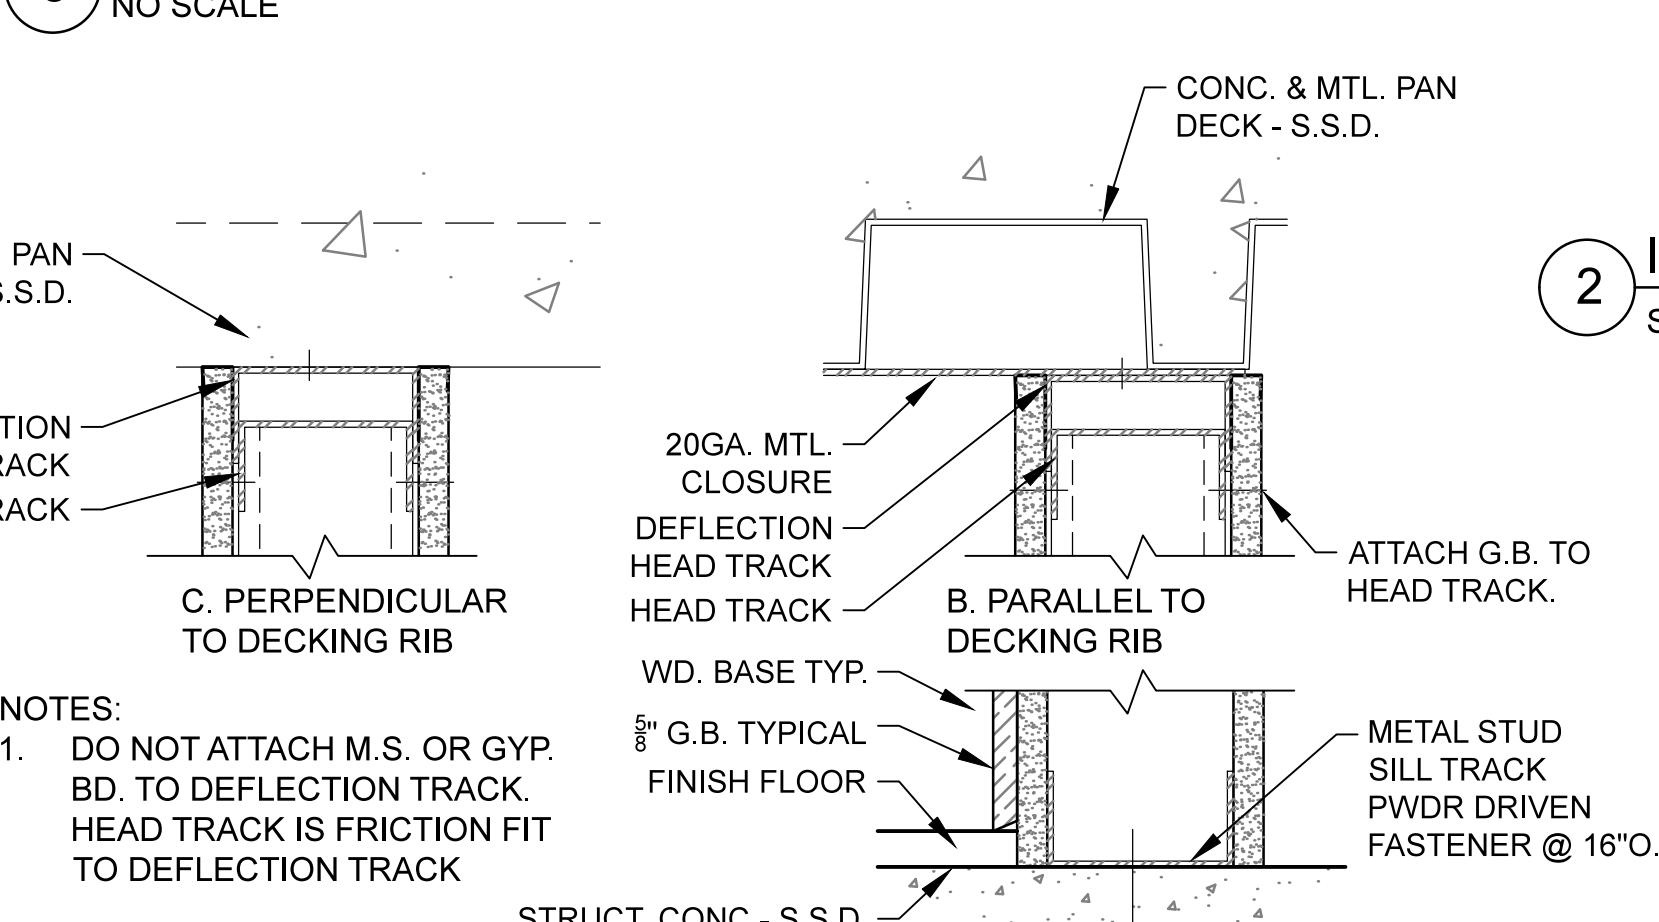


**INTERIOR ABUTTING WALLS - TYPICAL**

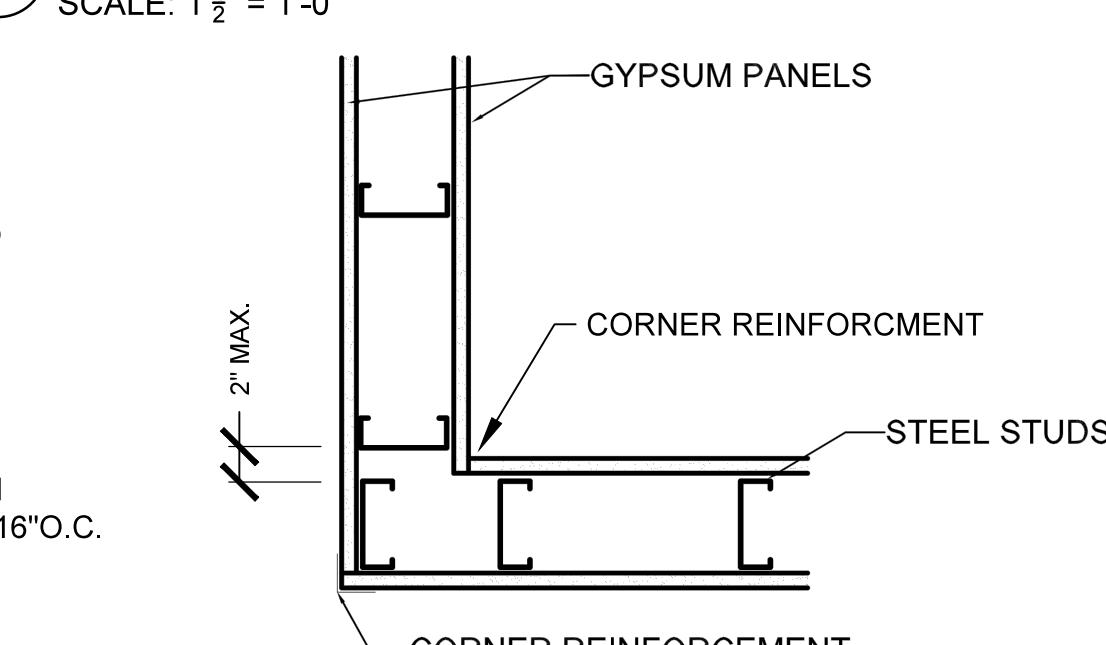

**TYPICAL INTERIOR GYPSUM BOARD WALL CORNER**


**ENTRANCE 104 DETAILS**

SCALE:  $1\frac{1}{2}'' = 1'-0''$

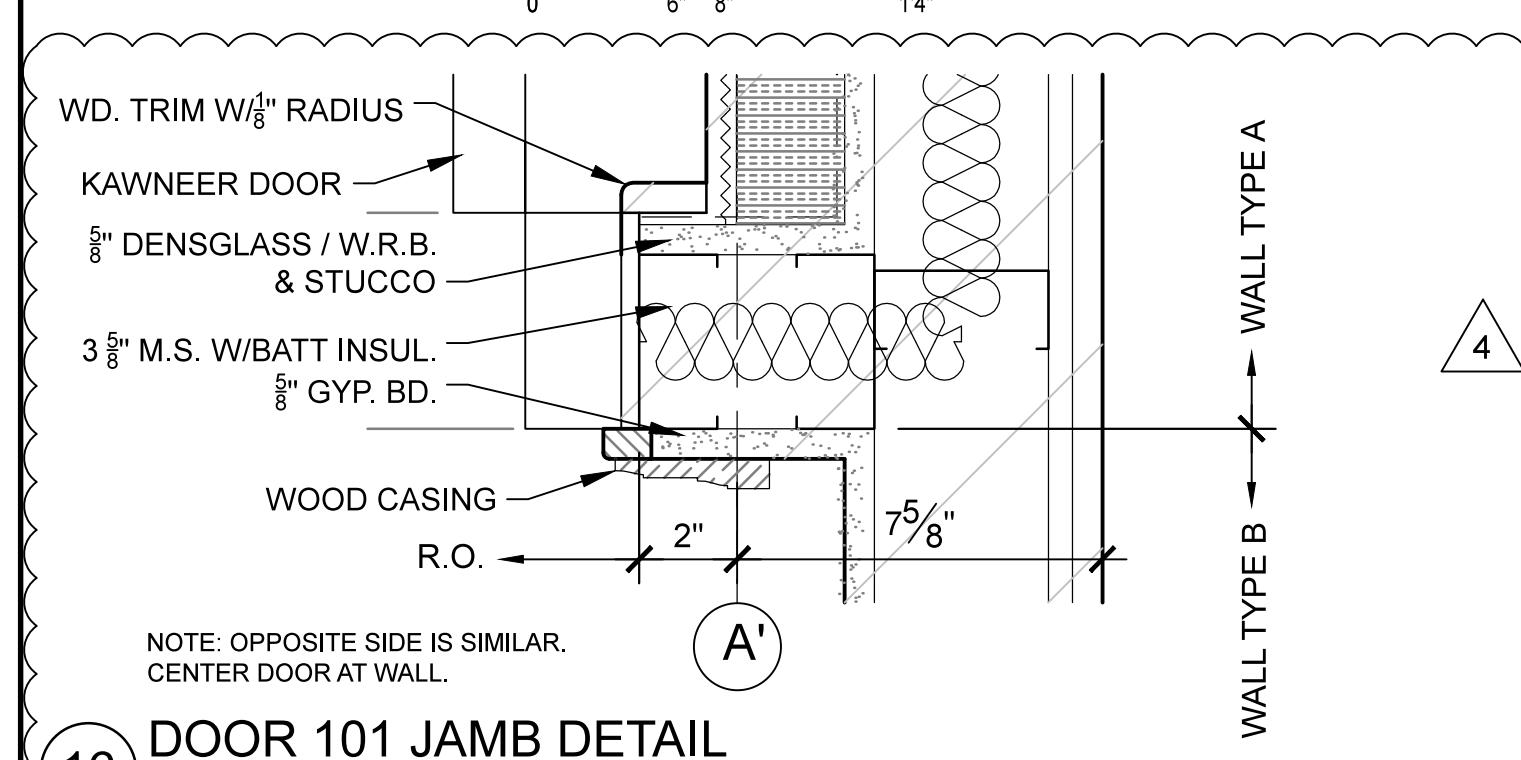

**DOOR 101 JAMB DETAIL**

SCALE:  $3'' = 1'-0''$

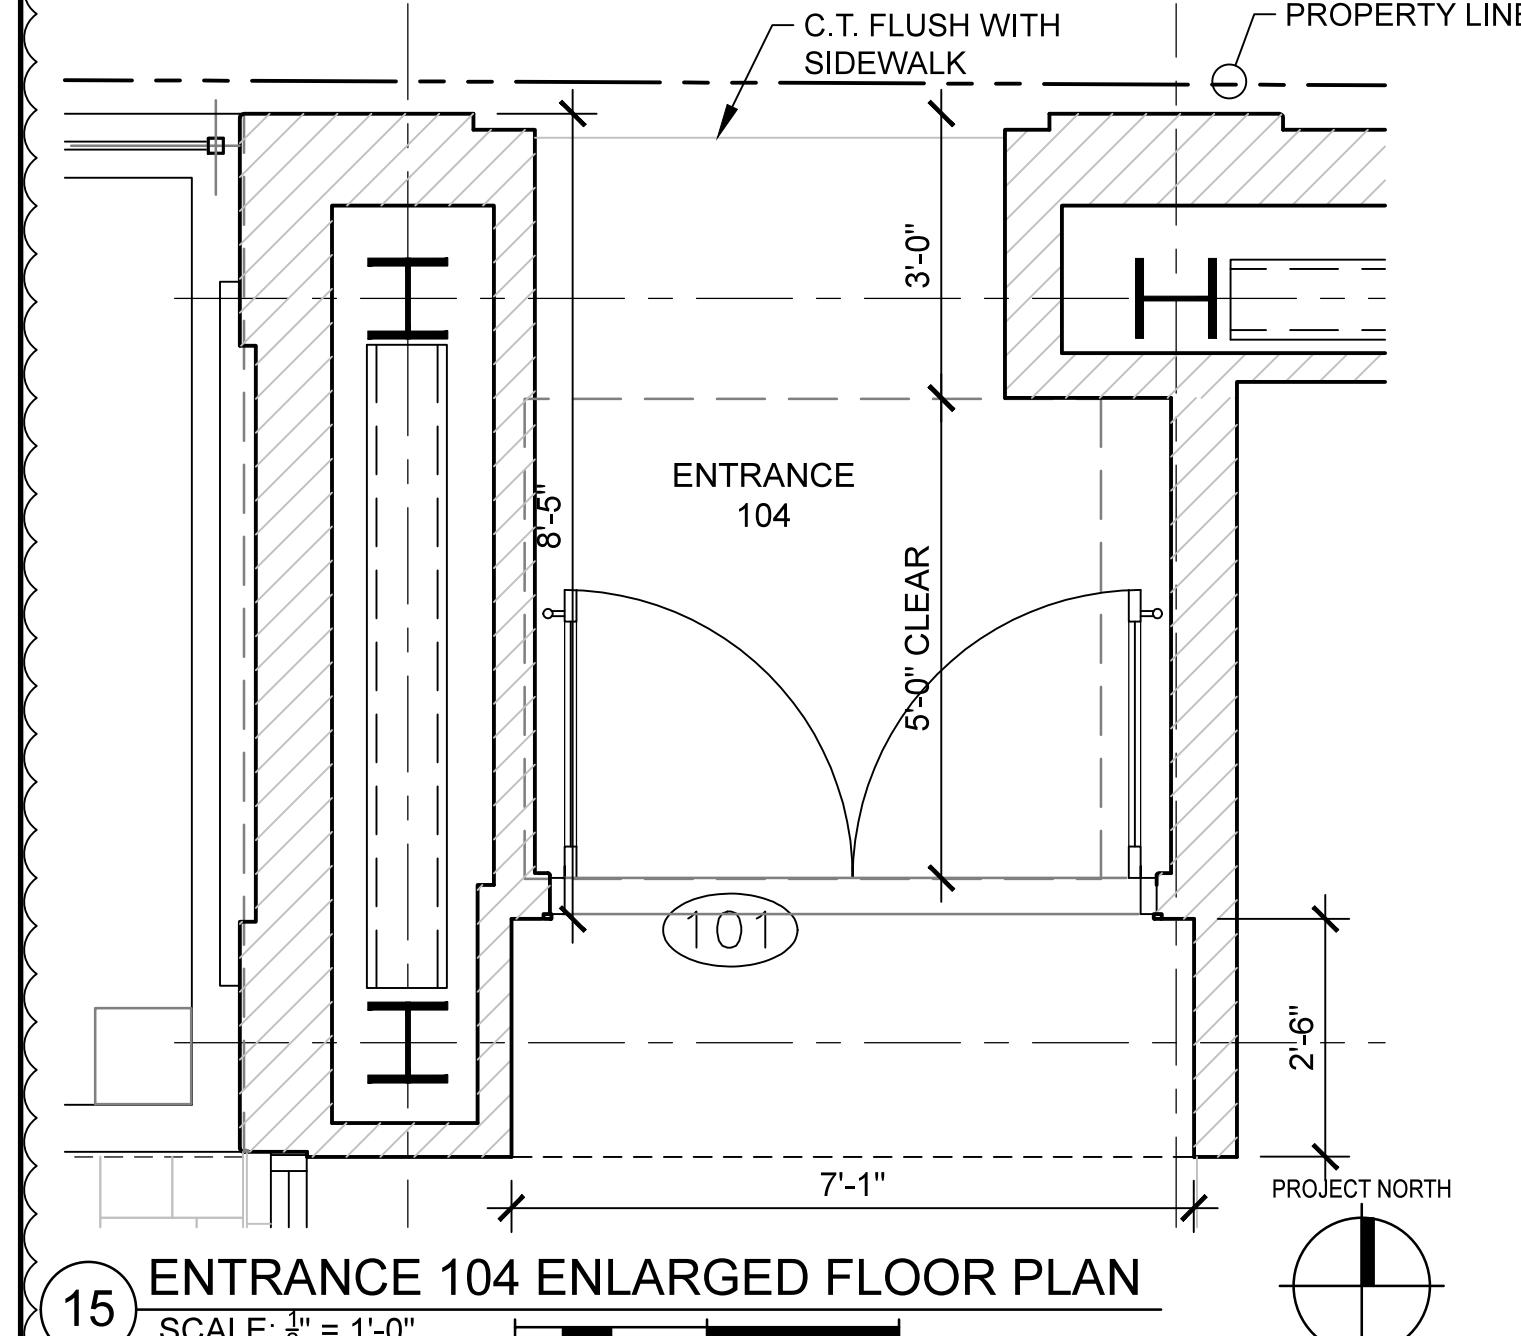


**ENTRANCE 104 ENLARGED FLOOR PLAN**

SCALE:  $\frac{1}{2}'' = 1'-0''$


**ENTRANCE 104 DETAILS**

SCALE:  $1\frac{1}{2}'' = 1'-0''$

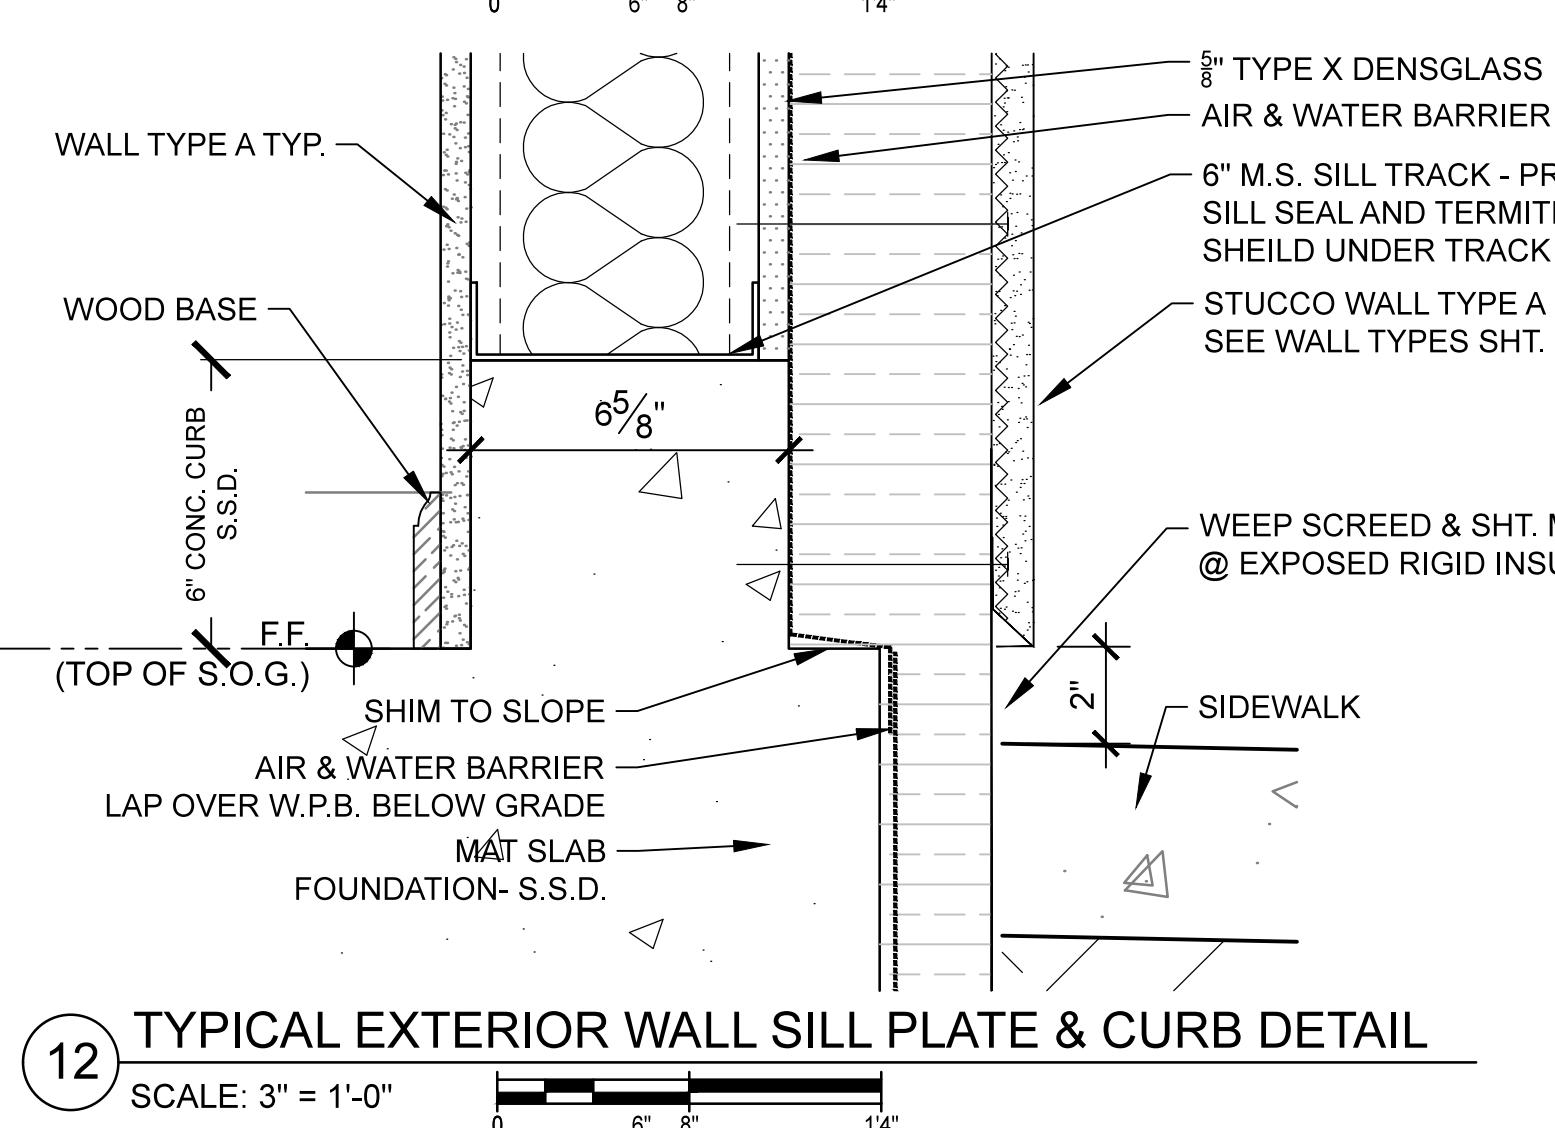

**Typical Exterior Wall Sill Plate & Curb Detail**

SCALE:  $3'' = 1'-0''$

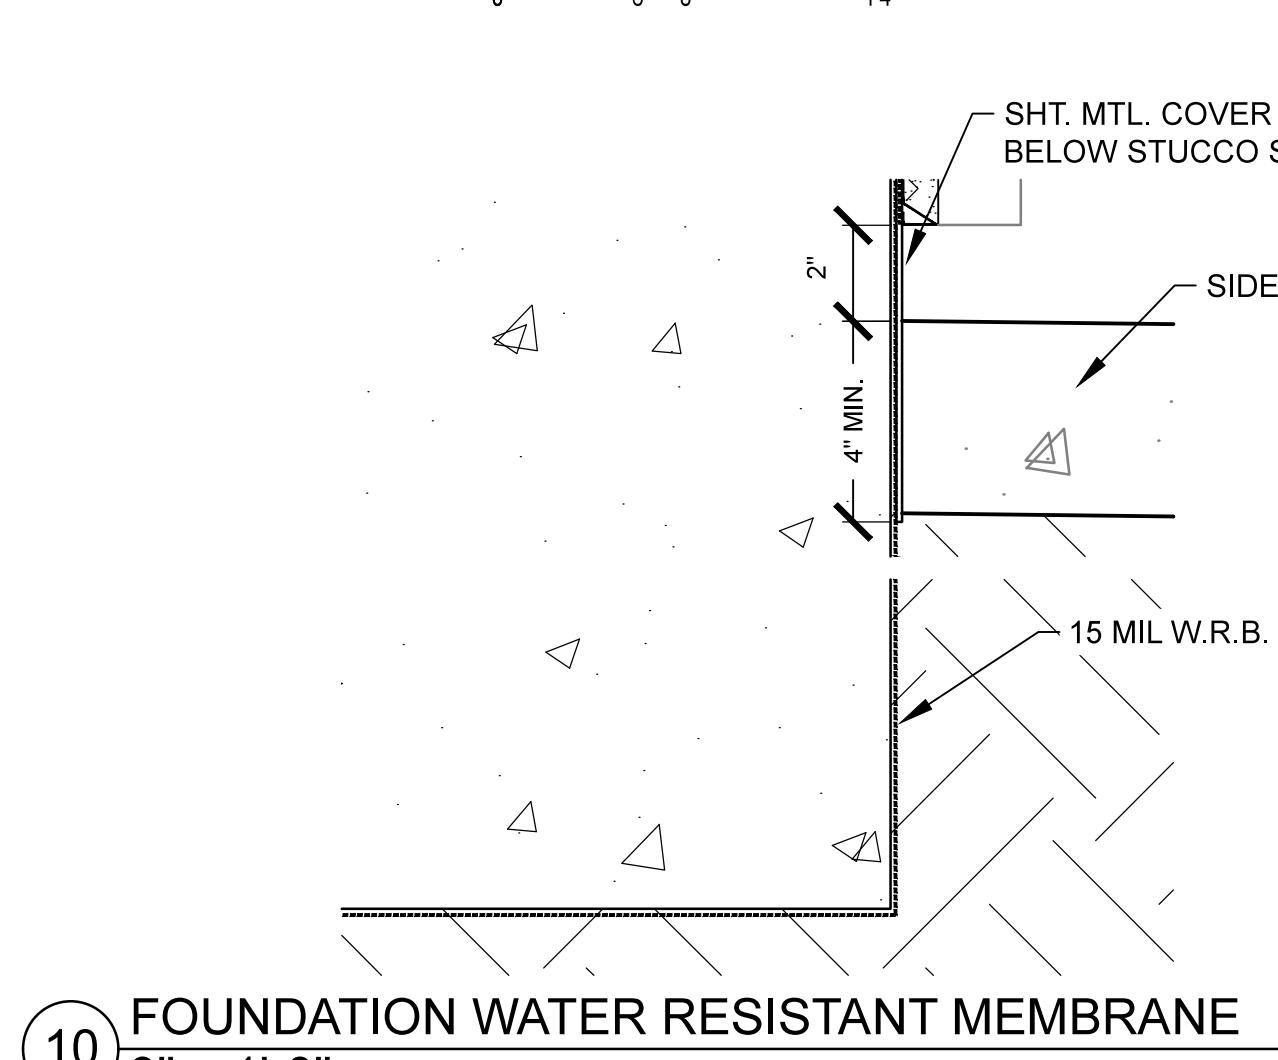


**FOUNDATION WATER RESISTANT MEMBRANE**

SCALE:  $3'' = 1'-0''$

**CHASE WALL METAL STUD BRACE**

NO SCALE

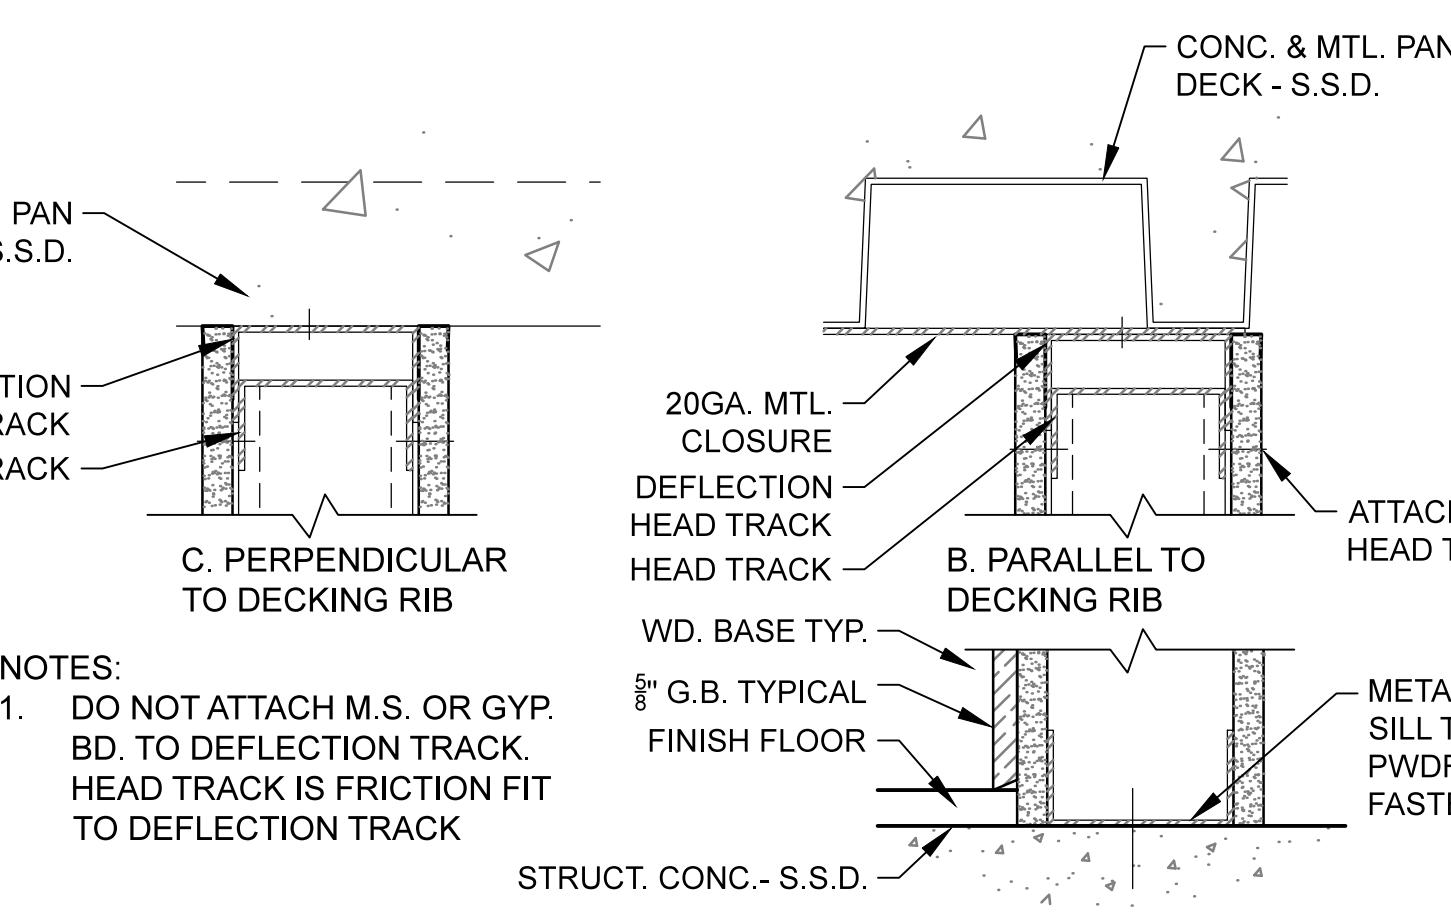

**TYPICAL INTERIOR WALL HEAD & SILL TRACK DETAILS**

SCALE:  $3'' = 1'-0''$

**A. SILL**

**1 TYPICAL INTERIOR GYPSUM BOARD WALL CORNER**

SCALE:  $1\frac{1}{2}'' = 1'-0''$