


Revision	
REV 1 PC comments 071723	
REV 2 PC comments 101623	
REV 3 PC comments 010224	
Clarification 040924	

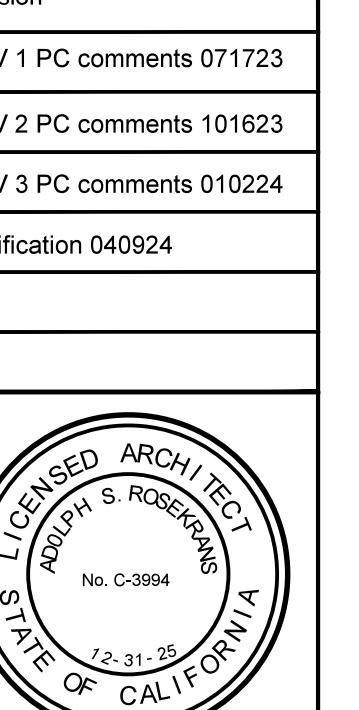

Architect  
Adolph S. Rosekrans, Inc.  
950 Runnymede Road  
Woodside, CA 94062  
650.851.7201  
Fax 650.851.7202  
rosekrans@pacbell.net

## WALL OPENING DETAILS & MISCELLANEOUS DETAILS

TAUBE FAMILY CARRIAGE HOUSE  
San Mateo County History Museum  
MUSEUM ADDITION  
San Mateo County Historical Association  
2200 Broadway Redwood City, CA 94063  
APN: 052-367-010  
Date 12-20-2022  
Scale U.O.N. AS NOTED  
Job 1702

A5.1

Sheet

### VAPRO SHIELD STANDARD WINDOW FLASHING DETAIL

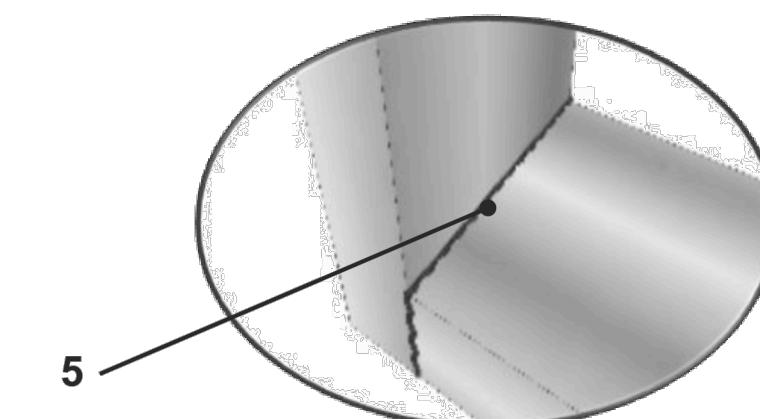


Figure 1, Close-up of corner

1. WrapFlashing SA Self-Adhered sill piece applied directly to sheathing + folded 2.75" inside of R.O. Leave release film on lower 6" to shingle over field membrane.

2. WrapFlashing SA Jamb Pieces applied directly to sheathing + folded 2.75" inside R.O.


3. WrapFlashing SA head piece applied directly to sheathing + folded 2.75" inside of R.O.

4. Vapro-SS Flashing installed in shingle fashion (sill, jambs, head) with 3" up-turned legs at sill and head + 1" on face; jambs are 1" onto the face.

5. VaproBond or VaproLiqui-Flash 1/2" tooled fillet bead at each corner where inside of R.O. meets face of sheathing. Ref. Figure 1.

6. Window installation and sealant joints + backer rod (by others)

7. Head flashing (by others) over Vapro-SS Flashing + embedded in VaproBond.

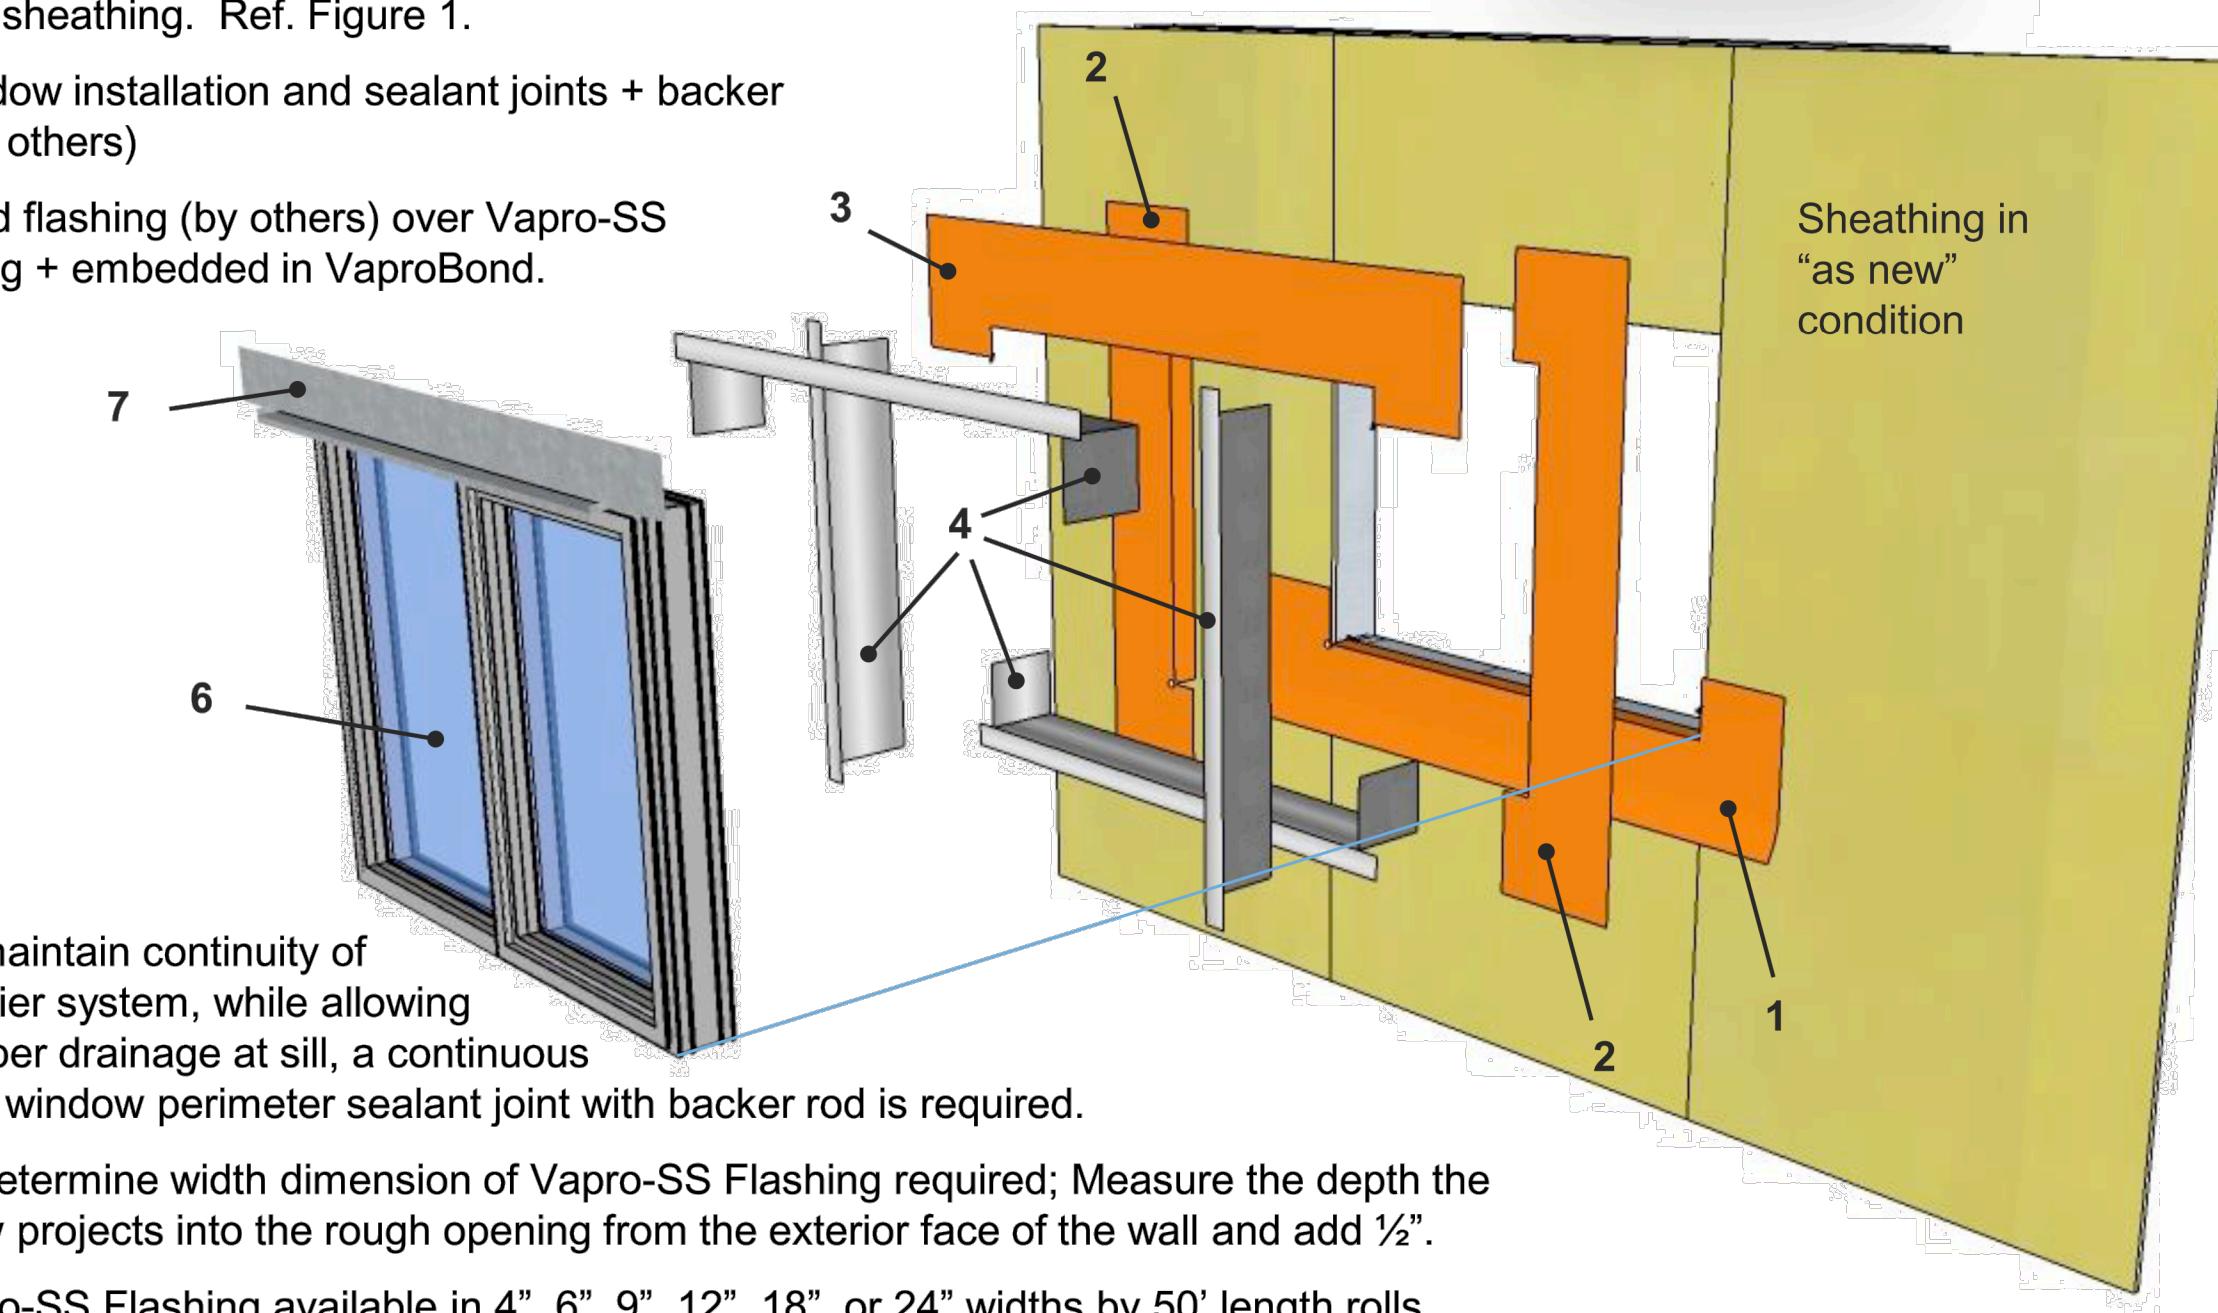


#### Notes:

a. To maintain continuity of air barrier system, while allowing for proper drainage at sill, a continuous interior window perimeter sealant joint with backer rod is required.


b. To determine width dimension of Vapro-SS Flashing required; Measure the depth the window projects into the rough opening from the exterior face of the wall and add 1/2".

c. Vapro-SS Flashing available in 4", 6", 9", 12", 18", or 24" widths by 50' length rolls

### TYPICAL WINDOW FLASHING

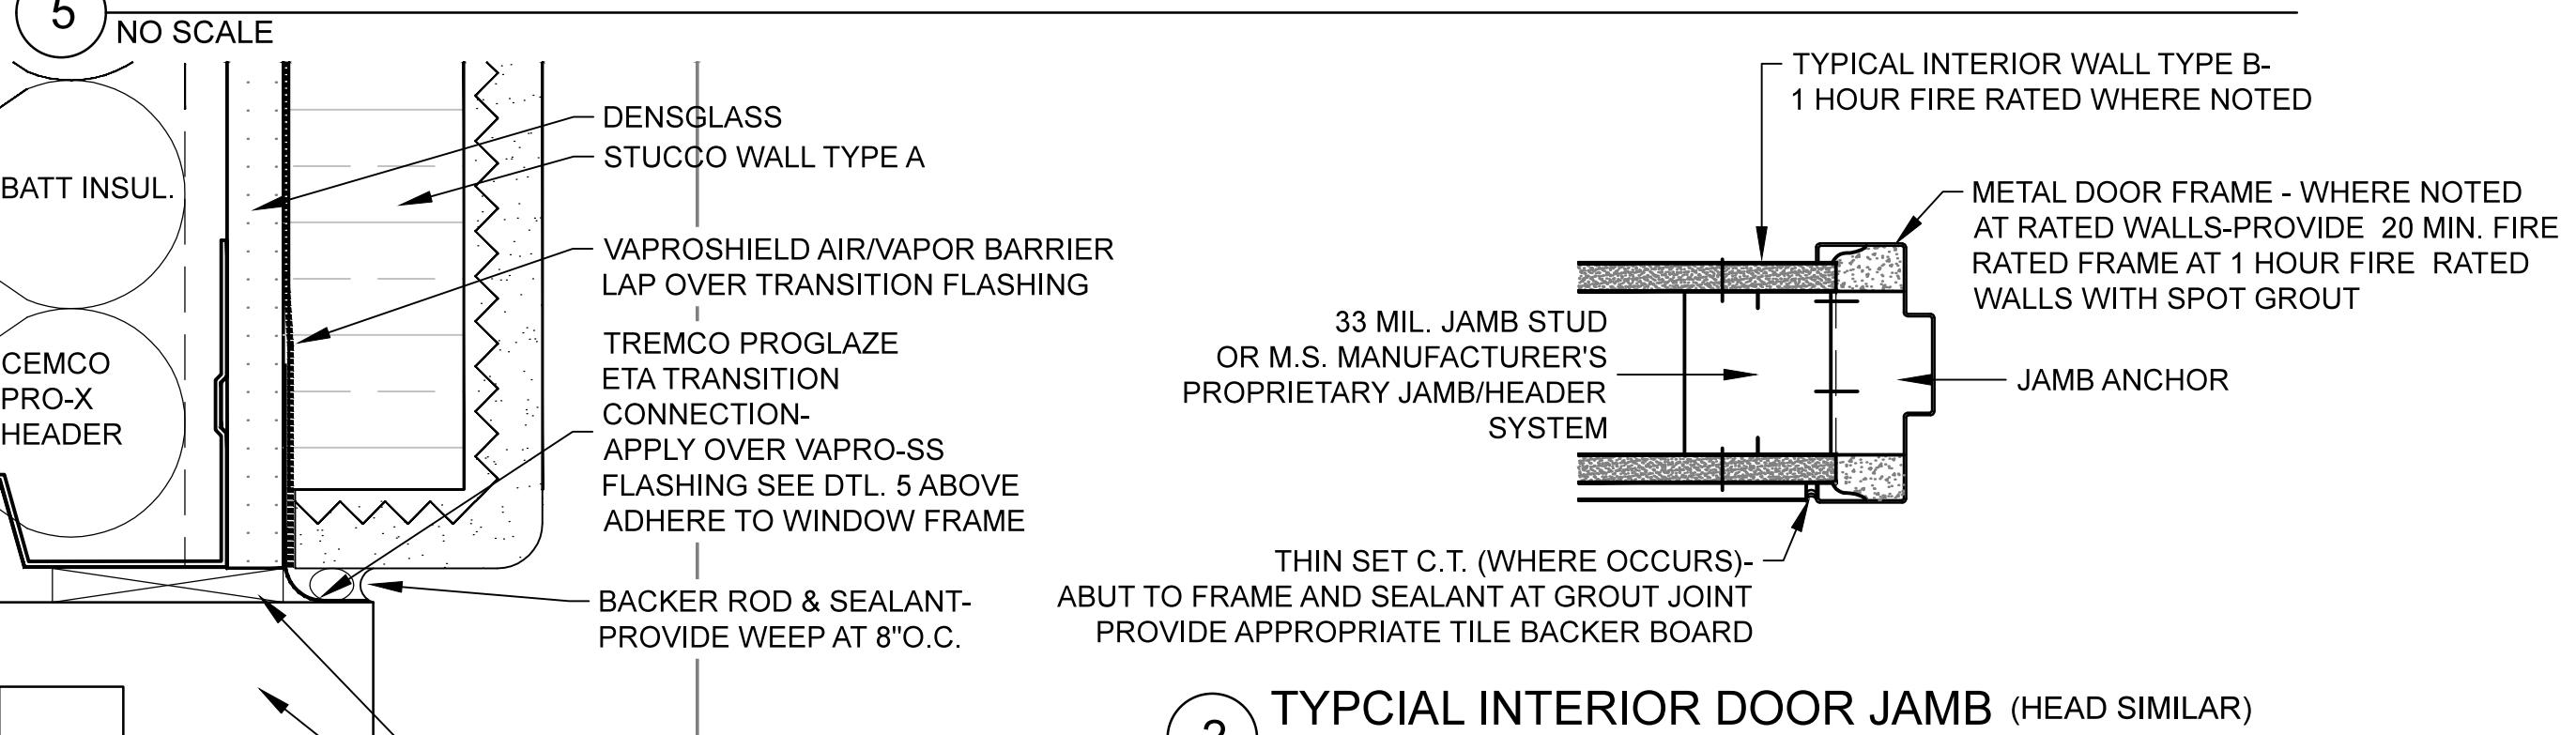

### TYPICAL INTERIOR DOOR JAMB (HEAD SIMILAR)

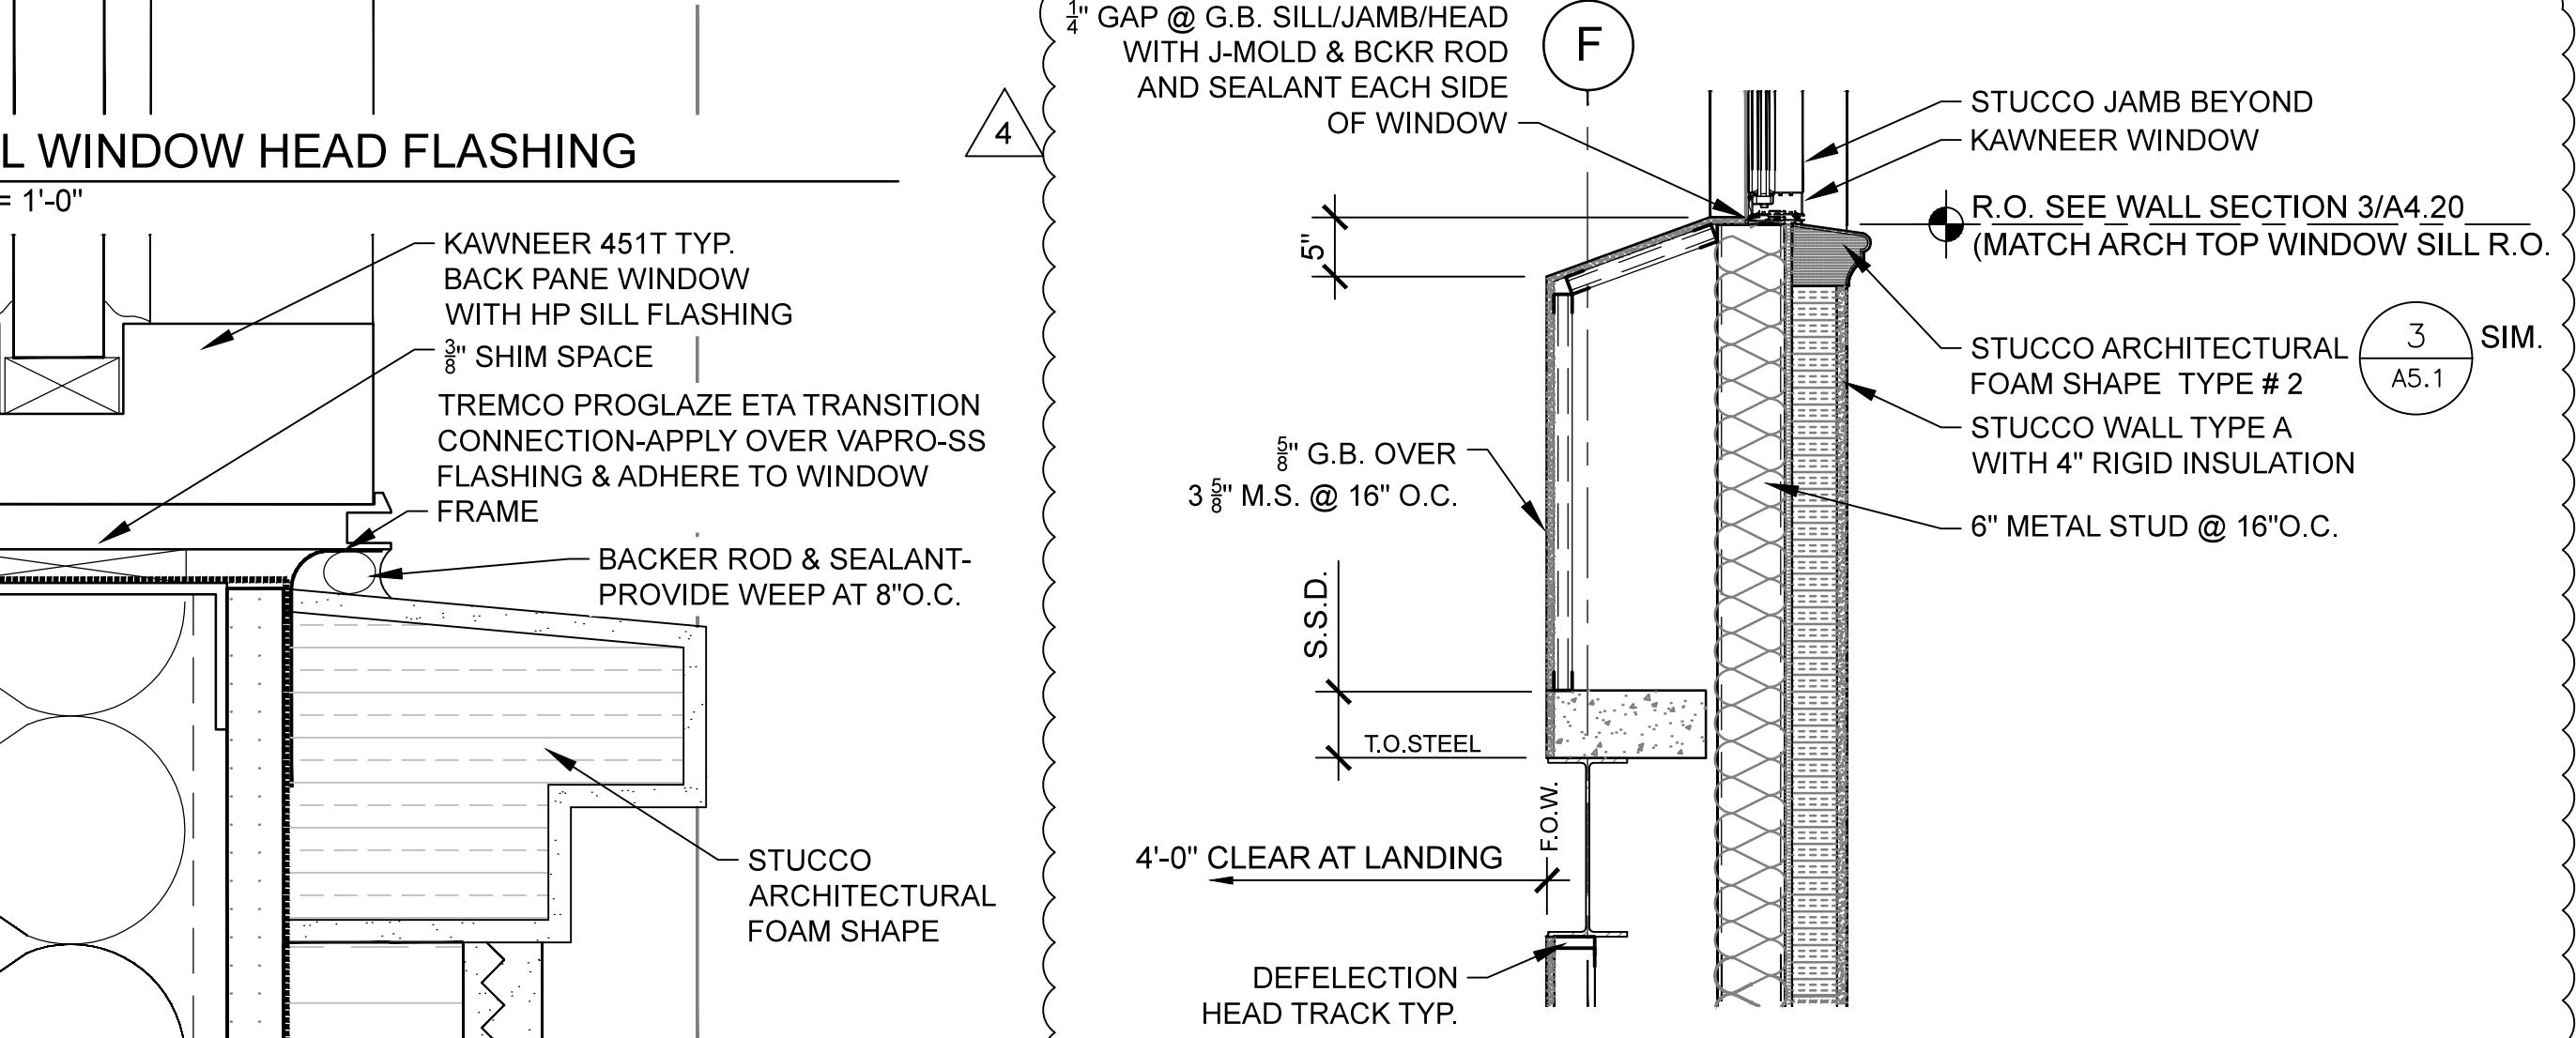

### SILL DETAIL WINDOW #308

SCALE: 3/4" = 1'-0"

0 1'-0" 2'-0"

1

2

3

4

5

6


7

8

9

10

11

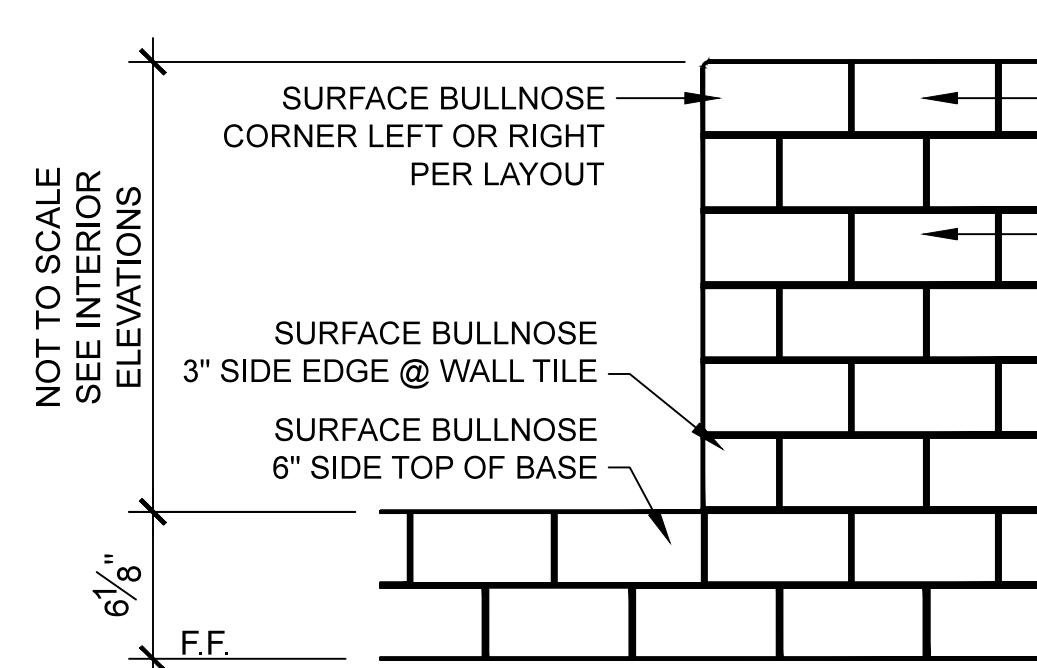

1

2

